REGION NO.	STATE	FED. AID PROJECT NO.	SHEET NO.
10	WASH.	~~F-011-2(~~ F-104()	

SEE SHEET 4 FOR PEDESTRIAN ACCESS NOTE

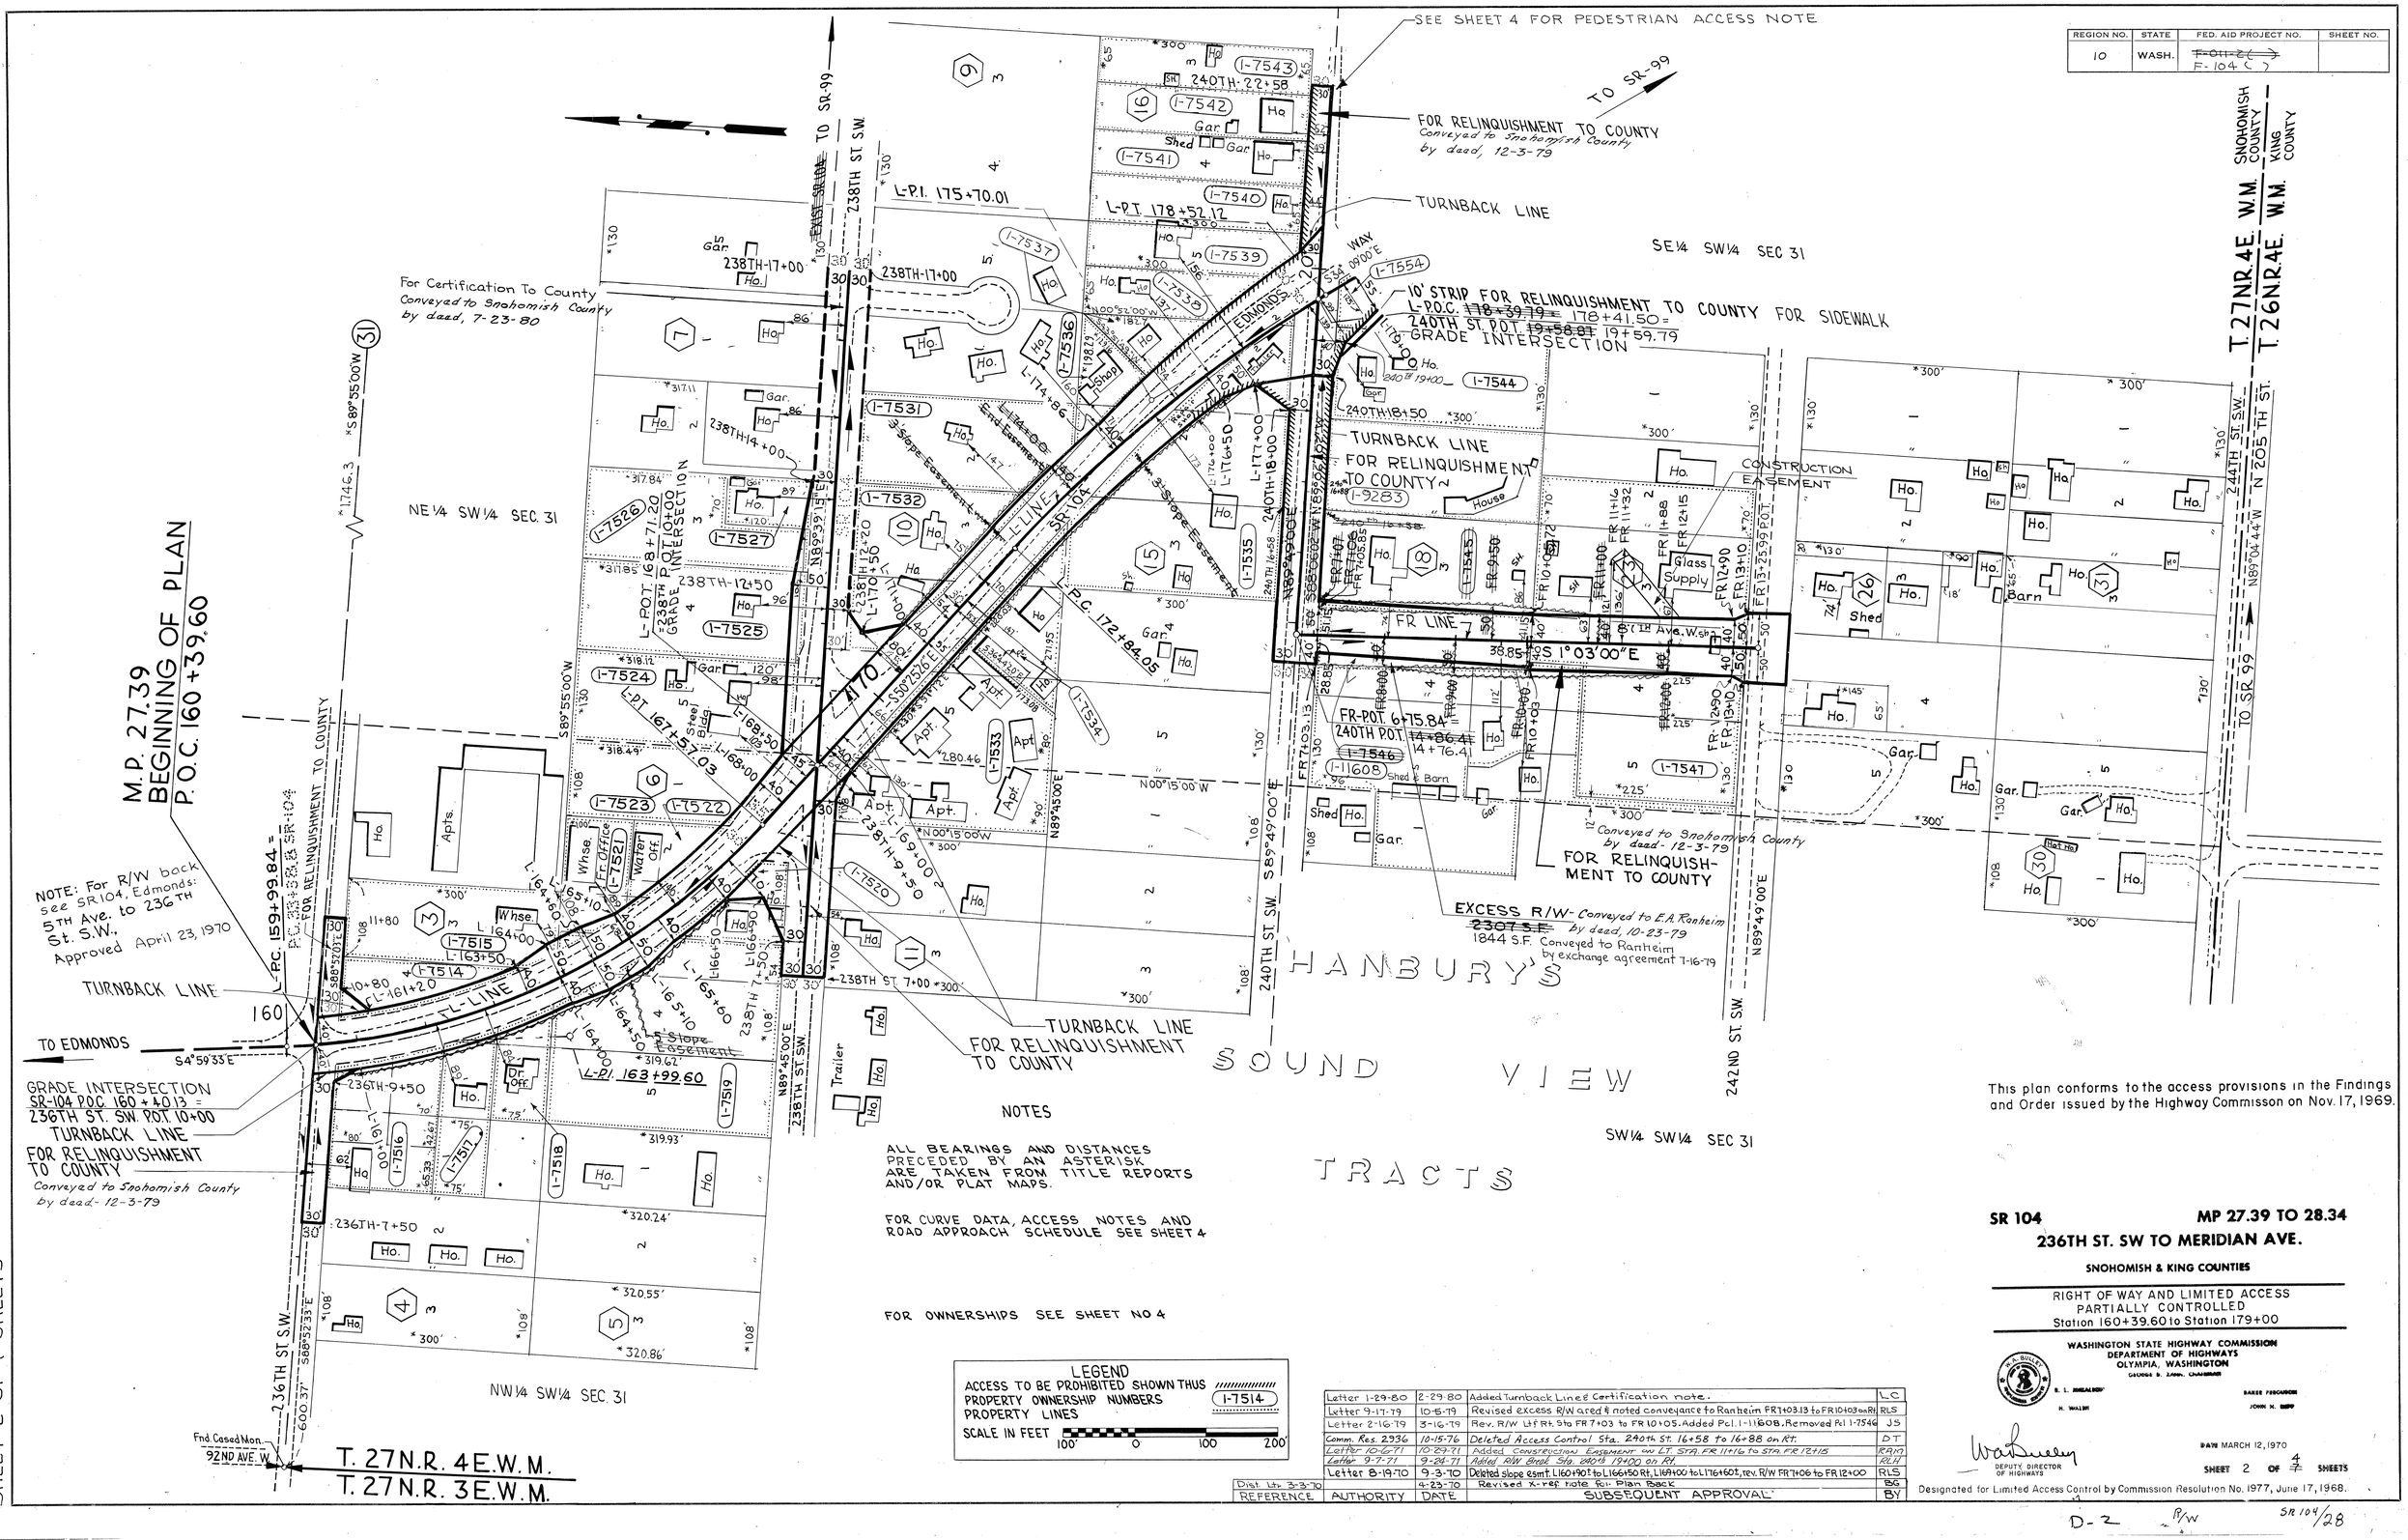

This plan conforms to the access provisions in the Findings and Order issued by the Highway Commisson on Nov. 17, 1969.

NOTES

ALL BEARINGS AND DISTANCES PRECEDED BY AN ASTERISK ARE TAKEN FROM TITLE REPORTS AND/OR PLAT MAPS.

FOR CURVE DATA, ACCESS NOTES AND ROAD APPROACH SCHEDULE SEE SHEET 4

FOR OWNERSHIPS SEE SHEET NO 4

LEGEND

ACCESS TO BE PROHIBITED SHOWN THUS
PROPERTY OWNERSHIP NUMBERS (1-7514)
PROPERTY LINES
SCALE IN FEET 100' 0 100 200'

REFERENCE	AUTHORITY	DATE	SUBSEQUENT APPROVAL	BY
			Revised X-ref note for Plan Back	BG
Dist. Ltr. 3-3-70		4-23-70		
Letter 8-19-70		9-3-70	Deleted slope esmt. L160+90± to L166+50 Rt, L169+00 to L176+60±, rev. R/W FR 7+06 to FR 12+00	RLS
Letter 9-7-71		9-24-71	Added R/W Break Stg. 240th 19+00 on Rt.	RLJ
Letter 10-6-71		10-29-71	Added CONSTRUCTION EASEMENT on LT. STA. FR 11+16 to STA. FR 12+15	RAM
Comm. Res. 2936		10-15-76	Deleted Access Control Sta. 240th St. 16+58 to 16+88 on Rt.	DT
Letter 2-16-79		3-16-79	Rev. R/W Lt Rt. Sta FR 7+03 to FR 10+05. Added Pcl. 1-11608. Removed Pcl 1-7546	JS
Letter 1-29-80		2-29-80	Added Turnback Line & Certification note.	LC

DEPUTY DIRECTOR OF HIGHWAYS

DATE MARCH 12, 1970

SHEET 2 OF 4 SHEETS

Designated for Limited Access Control by Commission Resolution No. 1977, June 17, 1968.

SR 104 **MP 27.39 TO 28.34**

236TH ST. SW TO MERIDIAN AVE.

SNOHOMISH & KING COUNTIES

RIGHT OF WAY AND LIMITED ACCESS PARTIALLY CONTROLLED
Station 160+39.60 to Station 179+00

WASHINGTON STATE HIGHWAY COMMISSION
DEPARTMENT OF HIGHWAYS
OLYMPIA, WASHINGTON

GEORGE B. LOWN, CHAIRMAN
R. L. ANDERSON
BAKER FERGUSON
R. WALLER
JOHN N. BERG

PARCEL NUMBERS F1314-F1615 HAVE BEEN ASSIGNED TO THIS PROJECT.

C.S.	A	Project	P	Acty	Unit	Gp
3430	D	L3242	A	240	10	09
3748	U					

DATE	BY	ALIGNMENT CHECKED
		RIGHT OF WAY " "
		GRADES " "
		BRIDGE " "
		STRUCTURE NOTATIONS " "

DRAWN	MURRAY - HACHTEL
TRACED	
CHECKED	Erickson
CHIEF ENGR.	
DIST. ENGR.	

SNOHOMISH COUNTY
L 3242 12063 BO

SHEET 2 OF 7 SHEETS

D-2 R/W SR 104/28