REGION NO.	STATE	FED. AID PROJECT NO.	SHEET NO.
10	WASH.	F-104( )	

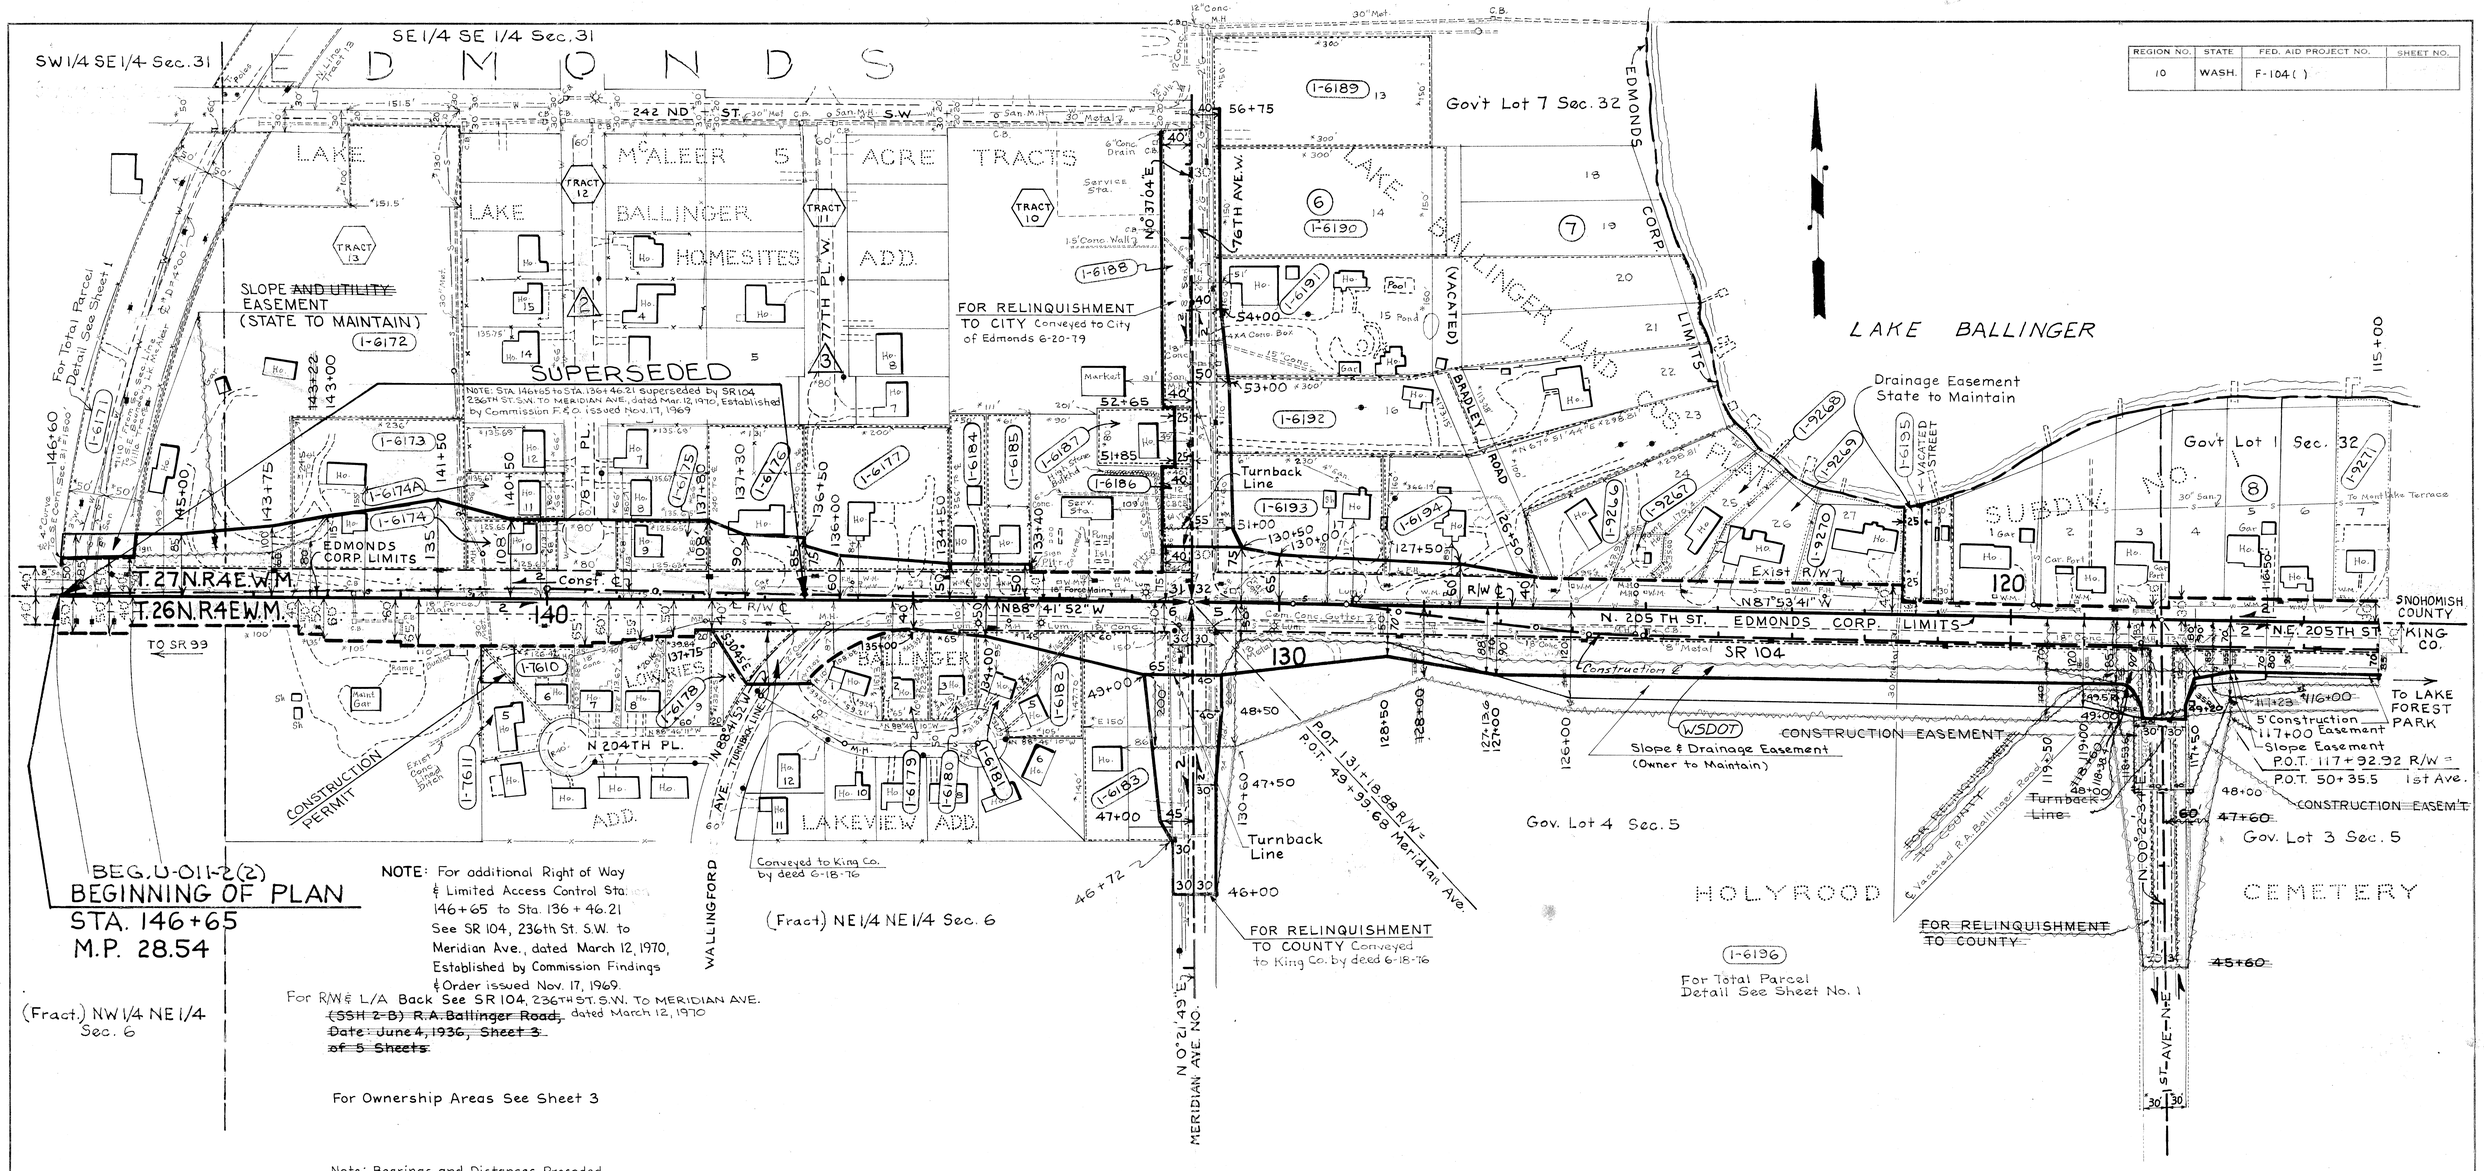

Letter 10-20-87	11-6-87	Deleted Turnback Line & Reling. note vic. 118+00 Lt.; Rev. R/W as acq. on Lt. 118+38.4 to 130+80±; Deleted Slope Esmt on Lt. 127+13.6 to 128+50.	DRS
Letter 10-20-77	Cal. 10-21-77	Rev. 8-14-79 Noted property conveyed to Edmonds by deed 6-20-79	RLS
Letter 7-20-76	8-6-76	Sta. 146+65 to Sta. 136+46.21 superseded and note added; noted property conveyed to King Co. by deed 6-18-76, added relinquishment to county 1st Ave. N.E.	RLS
Letter 5-10-76	6-4-76	Deleted utility from slope easement Sta. 145+60± to Sta. 146+60 on Rt.	RLS
Comm. F.&O. 11-17-69	1-23-70	Note added for Sta. 146+65 to Sta. 136+46.21 R/W-L/A Cross Reference	JDT
Ltrs. 11-13-69 & 1-6-70	1-15-70	Revised turnback line 76th Ave. W. added turnback line 1st Ave. N.E., permit Sta. 141 on So.	RLS
Letter 7-21-69	7-23-69	Revised R/W Sta. 136+46.21 to Sta. 145+60 Easement & Sh. 1 Revised Sheet 1 & 2 Parcel Added	L.C.
Letter 1-10-69	1-24-69	Deleted Easement & Revised R/W on No. Sta. 145+65± to Sta. 143+00	RLS
Letter 4-15-69	5-8-69	Added Easement & Revised R/W on No. Sta. 146+60 to Sta. 143+00	L.C.
Letter 1-30-68	10-31-68	Added R/W dimensions & Sta. prevous Sta. 118+58.6 to Sta. 111+25 on Rt.	R.L.S.
Letter 7-30-68	8-26-68	R/W Revised on Rt. Sta. 119+50 to Sta. 115+00 Easm't Added on Rt. Sta. 119+00 to Sta. 116+00	L.C.
AUTHORITY	DATE	SUBSEQUENT APPROVAL	BY

LEGEND

PROPERTY OWNERSHIP NUMBERS (1-6171)

PROPERTY LINES

100 60 30 0 100 200

SCALE IN FEET

SR 104

MP 28.54 TO MP 29.42

SR 99 TO SR 5

KING AND SNOHOMISH COUNTIES

RIGHT OF WAY

STA. 146+65 TO STA. 115+00

WASHINGTON STATE HIGHWAY COMMISSION
DEPARTMENT OF HIGHWAYS
OLYMPIA, WASHINGTON

GEORGE D. ZAHN, CHAIRMAN

R. L. MIKALSON — BAKER FERGUSON

H. WALSH — JOHN N. RUPP

ASS'T. DIRECTOR FOR HIGHWAY DEVELOPMENT

APPROVED: DEC. 7, 1967

SHEET 2 OF ~~5~~ 3 SHEETS

CS 1748-U L-3242

SR-104/25

Sheet 2 of 5 Sheets