REGION NO.	STATE	FED. AID PROJECT NO.	SHEET NO.
8	WASH.	U-011-2(2)	3 of 5

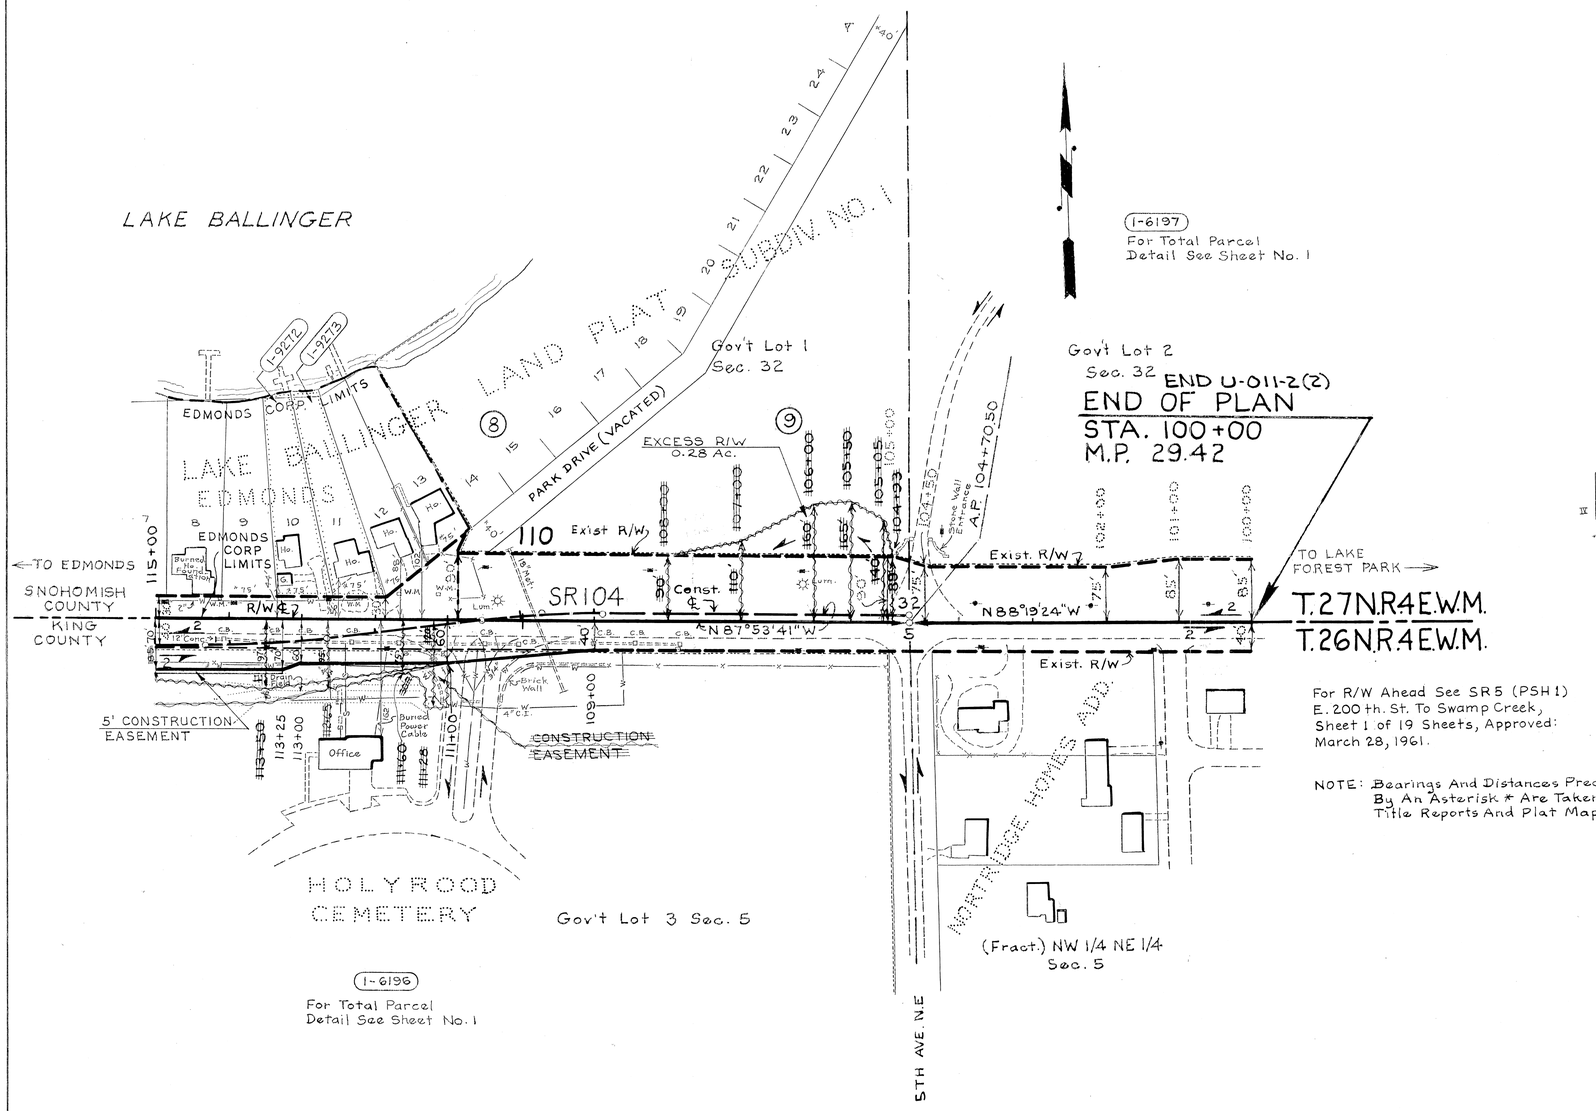

For R/W Ahead See SR 5 (PSH 1)
E. 200 th. St. To Swamp Creek,
Sheet 1 of 19 Sheets, Approved:
March 28, 1961.

NOTE: Bearings And Distances Preceded By An Asterisk * Are Taken From Title Reports And Plat Maps.

			OWNERSHIPS FOR SHEET NO. 2.				
		CONSTR. EASEMENT	PARCEL NO.	NAME	TOTAL AREA	TAKE	LT. REMAINDER RT.
	II	3,320 S.F.	1-6171	SNOHOMISH CO. P.U.D. NO. 1	100,000 S.F.	180 S.F.	99,820 S.F.
	III II		1-6172	BRANDT ET AL	168,000 S.F.	11,200 S.F.	156,800 S.F.
	III II		1-6173	BRANDT	48,380 S.F.	19,000 S.F.	29,380 S.F.
			1-6174	PIERSON	8,544 S.F.	8,544 S.F.	
			1-6175	HASKENS	8,544 S.F.	8,544 S.F.	
			1-6176	EDWARDS, J.	26,200 S.F.	6,750 S.F.	19,450 S.F.
			1-6177	EDWARDS, L.	40,000 S.F.	3,625 S.F.	36,375 S.F.
			1-6178	COLACURCIO	8,620 S.F.	4,210 S.F.	4,410 S.F.
			1-6179	CALLOWAY	7,920 S.F.	20 S.F.	7,900 S.F.
			1-6180	HIGDON	7,740 S.F.	330 S.F.	7,710 S.F.
			1-6181	PRICE	10,090 S.F.	2,740 S.F.	7,350 S.F.
			1-6182	TOLAND	10,065 S.F.	610 S.F.	9,455 S.F.
			1-6183	BRUNSON	34,520 S.F.	11,540 S.F.	22,980 S.F.
			1-6184	GEBHART	10,800 S.F.	500 S.F.	10,300 S.F.
			1-6185	PRUDENTIAL MUTUAL	13,176 S.F.	610 S.F.	12,566 S.F.
			1-6186	CITY OF EDMONDS	5,840 S.F.	5,840 S.F.	
			1-6187	MACKIE	10,400 S.F.	2,000 S.F.	8,400 S.F.
			1-6188	CITY OF EDMONDS	15,360 S.F.	15,360 S.F.	
			1-6189	BEESON	45,000 S.F.	550 S.F.	44,450 S.F.
			1-6190	CARLSON	48,000 S.F.	1,500 S.F.	46,500 S.F.
			1-6191	PATTERSON	97,080 S.F.	2,050 S.F.	95,030 S.F.
			1-6192	QUIGLEY	37,870 S.F.	2,100 S.F.	35,770 S.F.
			1-6193	LIGHT	36,800 S.F.	9,310 S.F.	27,490 S.F.
			1-6194	WHITE	56,070 S.F.	3,200 S.F.	52,870 S.F.
SLOPE & DRAIN. EASE.	SLOPE EASE.	CONSTR. EASEMENT	1-6195	Mc LAREN	9,450 S.F.	EASEMT ONLY. 3550 S.F.	
II 0.96 Ac.	0.034 Ac.	0.037 Ac.	1-6196	CATHOLIC BISHOP OF SEATTLE	152 Ac.	1.38 Ac.	150.62 Ac.
		CONSTR. PERMIT					
		II 1,125 S.F.	1-7610	YERKOVICH, ALETTA	8,190 S.F.		
		II 1,125 S.F.	1-7611	O'KEEFE, H.J. & SARAH L.	8,140 S.F.		
			1-6174A	REGAN	8,954 S.F.	540 S.F.	8,414 S.F.
		IV	1-9266	MURPHY	29,920 S.F.	DRIVEWAY	EASEMENT
		IV	1-9267	CITY OF MOUNTLAKE TERRACE	3,645 S.F.	"	"
		IV	1-9268	CONNER	11,500 S.F.	"	"
		IV	1-9269	ALEXANDER	15,340 S.F.	"	"
		IV	1-9270	BOTTEN	15,633 S.F.	"	"
		IV	1-9271	ERICKSON	20,820 S.F.	"	"

		OWNERSHIPS FOR SHEET NO. 3			
PARCEL NO.	NAME	TOTAL AREA	TAKE	LT. REMAINDER	RT.
1-6197	NILE TEMPLE	126.50 Ac.	0.28 Ac.		126.22 Ac.
IV 1-9272	SMITH	16,710 S.F.	DRIVEWAY	EASEMENT	
IV 1-9273	BERKEY	16,690 S.F.	"	"	

LEGEND
PROPERTY OWNERSHIP NUMBERS (1-6197)
PROPERTY LINES
100 60 30 0 100 200
SCALE IN FEET

Letter 4-24-87	5-8-87	Noted Excess R/W on Rt. 104+93 to 108+00.	DRS
Letter 11-13-69	1-16-70	Added Parcels 1-7610 & 1-7611	RLS
Letter 10-21-69	10-30-69	R/W Rev. on Rt. Sta. 104+93 to 108+00 & on Lt. Sta. 110+00 to 115+00; Areas Added & Revised	AEL
Letter 7-10-69	7-24-69	Revised Areas Parcels 1-6172 & 1-6173	RLS
Letter 4-15-69	5-8-69	Revised Areas on Parcels 1-6171, 1-6172, 1-6173	L.C.
Letter 1-30-68	10-31-68	Revised Areas Parcel 1-6196	R.L.S.
Letter 7-30-68	8-22-68	R/W Revised on Rt. Sta. 115+00 to Sta. 111+00. Const. Easement Added on Rt. vic. Sta. 110	L.C.
AUTHORITY	DATE	SUBSEQUENT APPROVAL	BY

SR 104
MP 28.54 TO MP 29.42
SR 99 TO SR 5
KING AND SNOHOMISH COUNTIES

RIGHT OF WAY
STA. 115+00 TO STA. 100+00

WASHINGTON STATE HIGHWAY COMMISSION
DEPARTMENT OF HIGHWAYS
OLYMPIA, WASHINGTON

GEORGE D. ZAHN, CHAIRMAN
V. L. MIKALSON
M. WALSH
BAKER FERGUSON
JOHN N. RUPP

ASS'T. DIRECTOR FOR HIGHWAY DEVELOPMENT

APPROVED: Dec. 7, 1967

SHEET 3 OF ~~5~~ 3 SHEETS

CS 1748-U L-3242

SR-104/25